Bergedorf Bille
Gemeinnützige Baugenossenschaft eG

Bündnis für das Wohnen und Klimaanpassung
Auftakt-Veranstaltung am 13.4.2023
BSW / BUKEA

RISA- Starkregenvorsorge – Praxisbeispiel aus Bergedorf

Johanna Sievers
SPALINK-SIEVERS Landschaftsarchitekten

www.spalink-sievers.de

SPALINK-SIEVERS LandschaftsArchitekten
BDLA, Hannover

Quartiersentwicklung Dünenweg/Lohbrügge

Bergedorf Bille
Gemeinnützige Baugenossenschaft eG

Quartiersentwicklung Dünenweg

Freianlagen - BESTAND

Planstand: 15.01.2023
Bearbeitung: St

o.M.
DIN A3

SPALINK-SIEVERS LandschaftsArchitekten PartG
Alte Herrenhäuser Str. 28
30419 Hannover
Tel. 0511 979 259 - 0
www.spalink-sievers.de

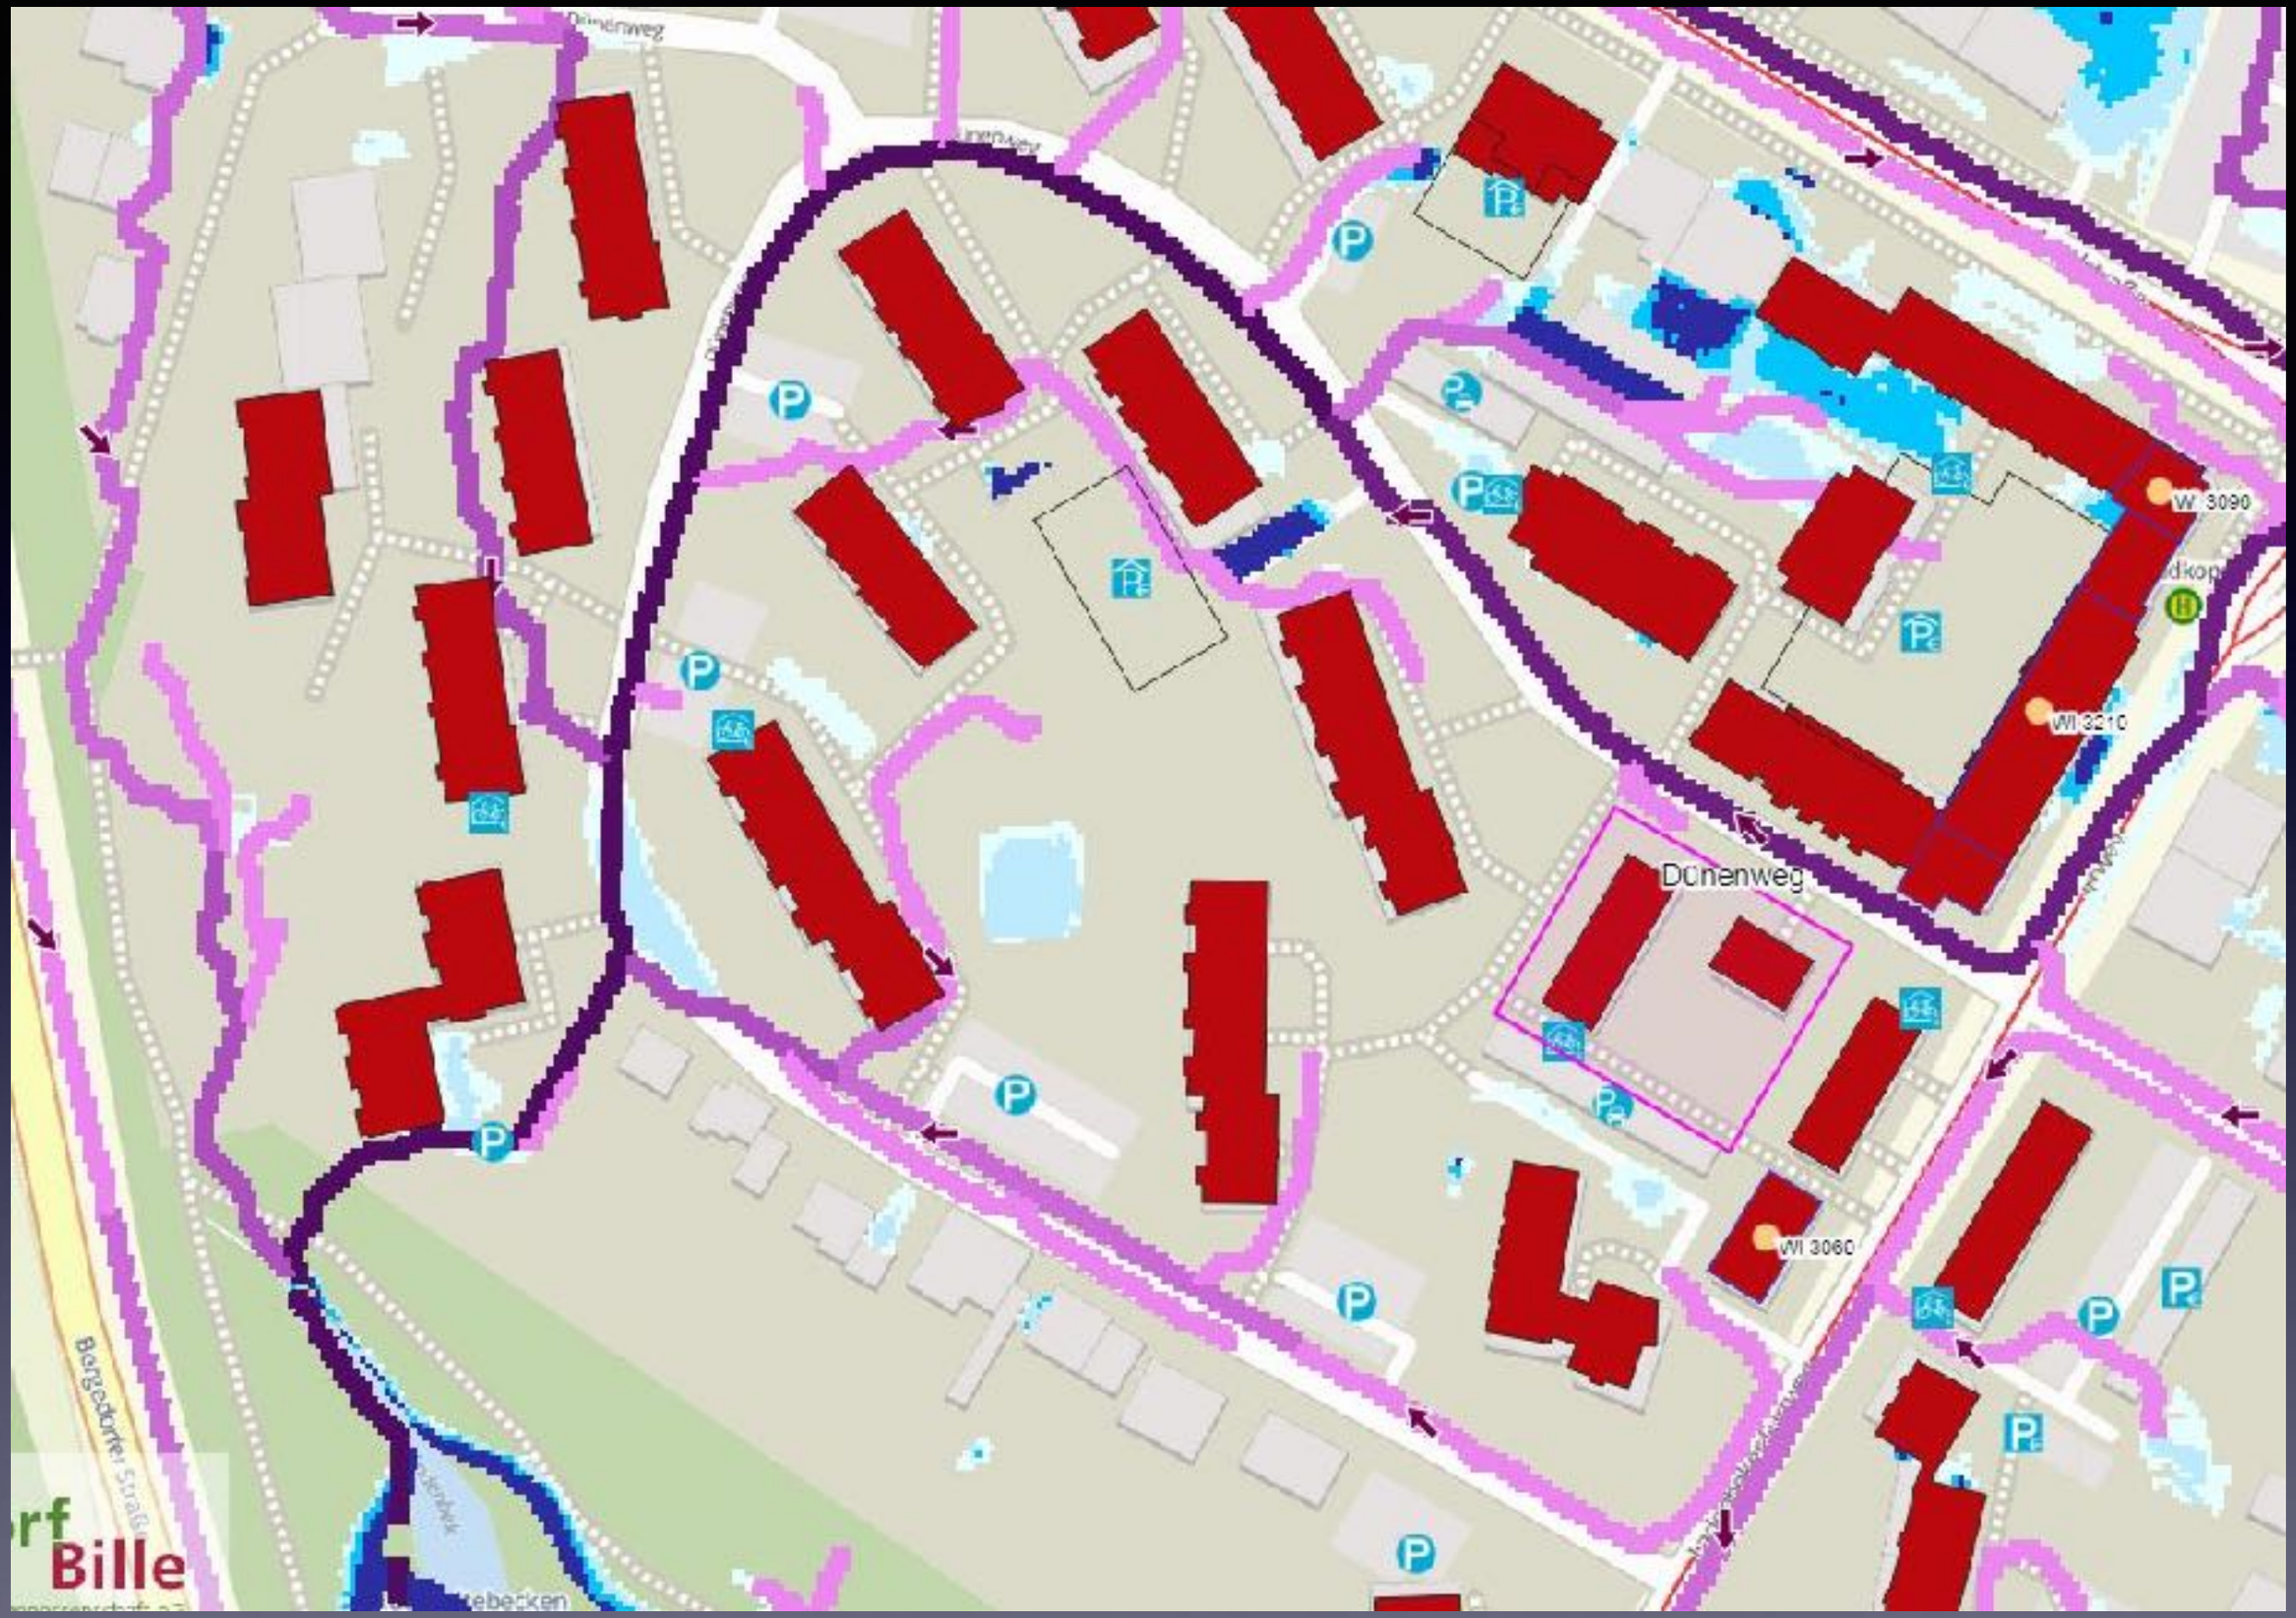

Starkregenhinweiskarte der Hansestadt Hamburg (Ausschnitt)

Dünenweg 74 /76:
Folgen des Starkregens am Himmelfahrtstag 2018

WILKO WAGNER

Entwässerungsplanung als Grundlage für die wasserrechtliche Erlaubnis zur Versickerung von Niederschlagswasser

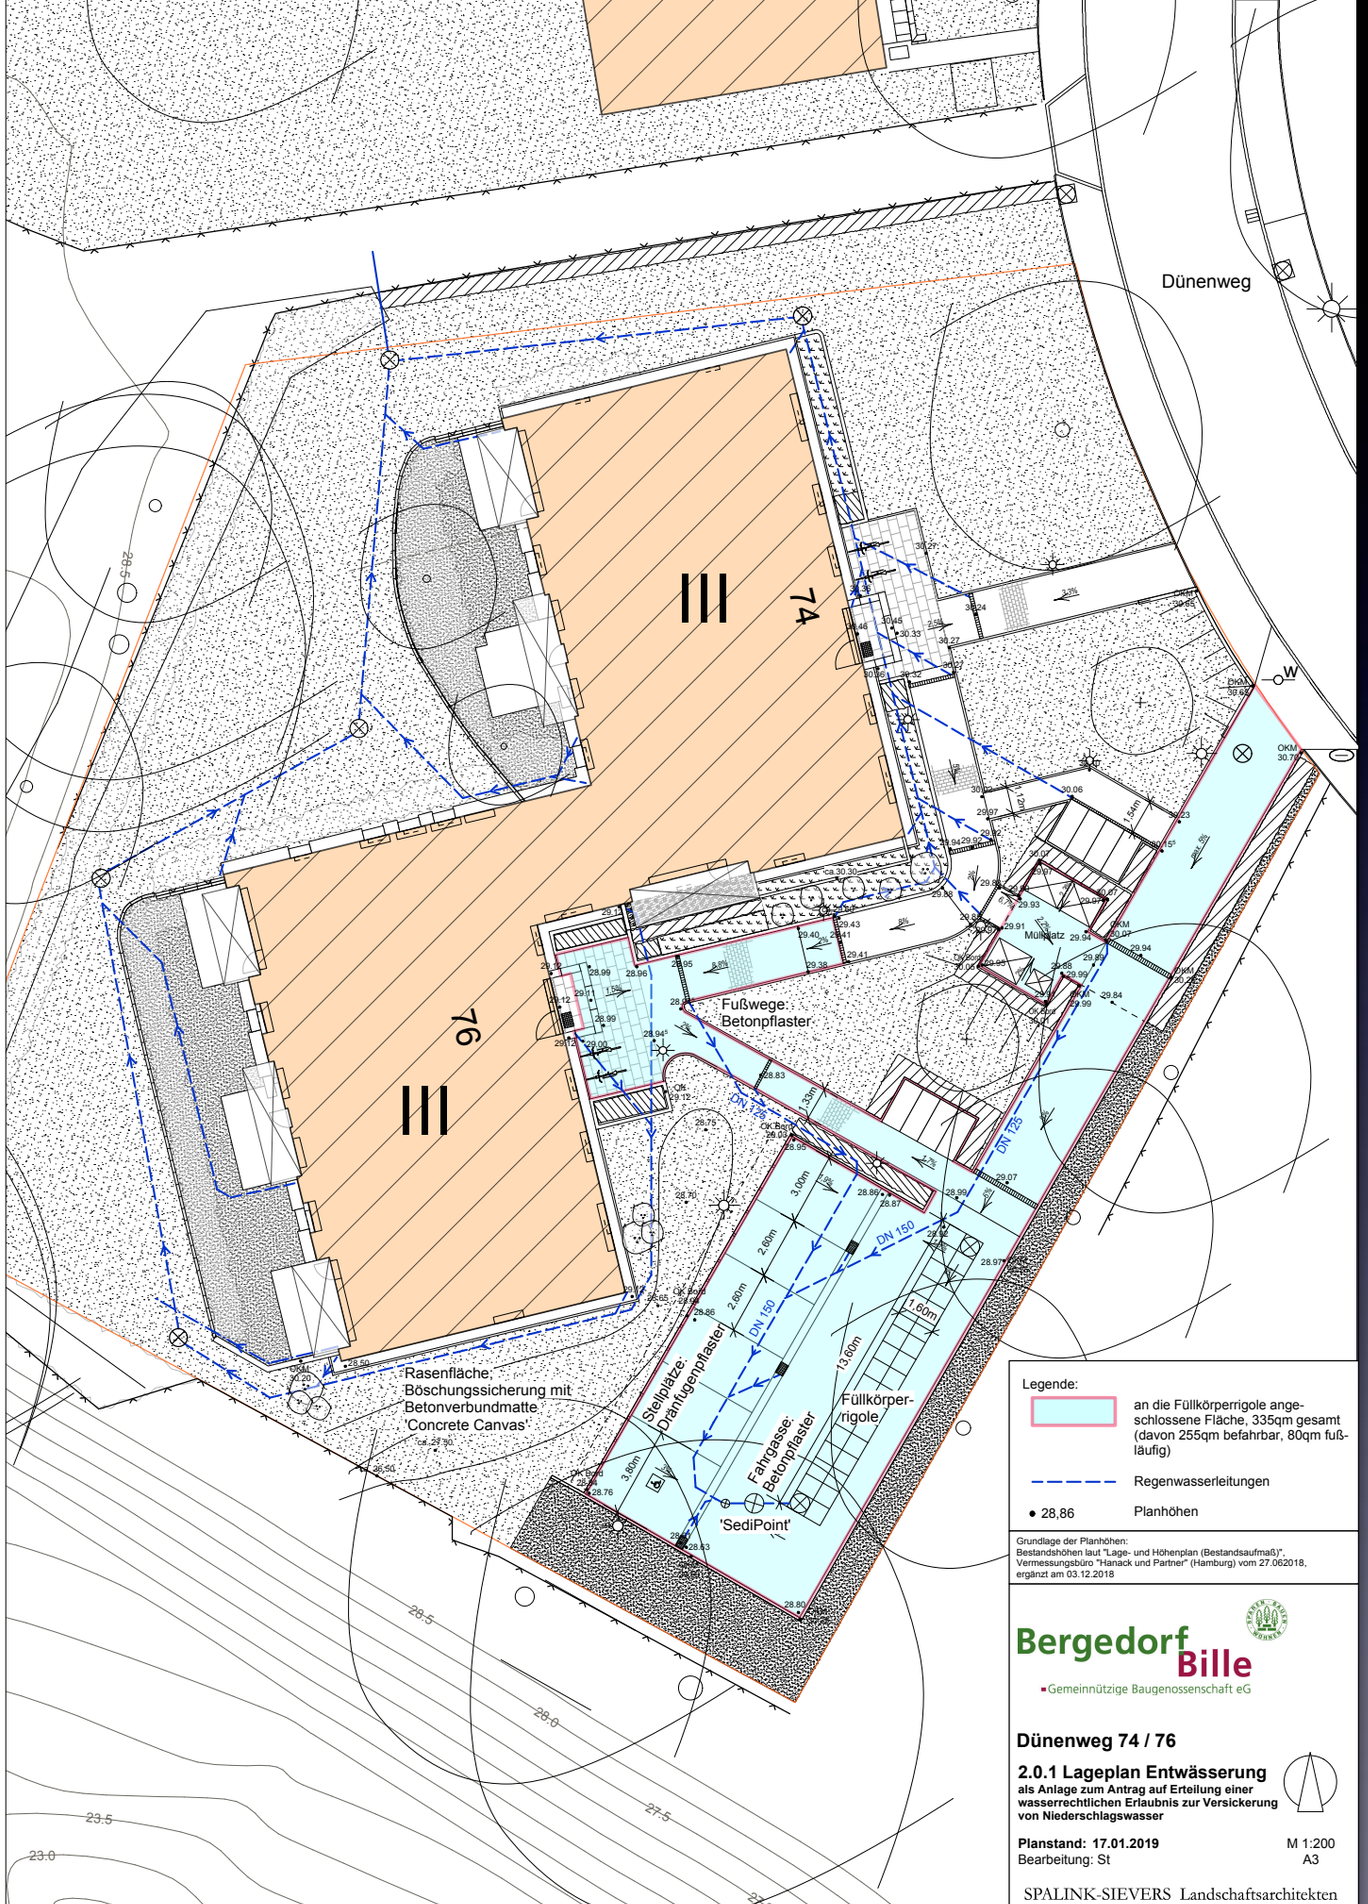

Legende:

- an die Füllkörperrigole angeschlossene Fläche, 335qm gesamt (davon 255qm befahrbar, 80qm fußläufig)
- Regenwasserleitungen
- • 28,86 Planhöhen

Grundlage der Planhöhen:
Bestandshöhen laut "Lage- und Höhenplan (Bestandsaufmaß)", Vermessungsbüro "Hanack und Partner" (Hamburg) vom 27.062018, ergänzt am 03.12.2018

Bergedorf Bille
Gemeinnützige Baugenossenschaft eG

Dünenweg 74 / 76

2.0.1 Lageplan Entwässerung
als Anlage zum Antrag auf Erteilung einer wasserrechtlichen Erlaubnis zur Versickerung von Niederschlagswasser

Planstand: 17.01.2019 M 1:200
Bearbeitung: St A3

SPALINK-SIEVERS Landschaftsarchitekten

Alte Herrenhäuser Str. 28 Tel. 0511 979 259 - 0
30419 Hannover www.spalink-sievers.de

Freie und Hansestadt Hamburg
Behörde für Umwelt und Energie

Behörde für Umwelt und Energie • Neuenfelder Straße 19 • 21109 Hamburg
Mit Empfangsbestätigung

Gemeinnützige Baugenossenschaft Bergedorf Bille e.G.
Bergedorfer Straße 118-122
21029 Hamburg

Eingang 15. Feb. 2019 Bergedorf-Bille eG

Amt Wasser, Abwasser und Geologie
Abteilung Wasserwirtschaft
- als Wasserbehörde -
Neuenfelder Straße 19
D-21109 Hamburg
Telefon 0 40 - 4 28 40 - 5288
Telefax 0 40 - 4279-40437
Ansprechpartner: Hella Franz
Raum: G.04.387
E-Mail: Hella.Franz@bue.hamburg.de

12. Februar 2019
Gz.: W1204 / 841.52-601/037

Wasserrechtliche Erlaubnis

1. Gemäß §§ 8 und 10 Abs. 1 in Verbindung mit § 9 Abs. 1 Nummer 4, § 12 Abs. 2 und § 13 des Gesetzes zur Ordnung des Wasserhaushaltes (Wasserhaushaltsgesetz WHG) vom 31. Juli 2009 (BGBl. I, 2009 Seite 2585ff) zuletzt geändert durch Artikel 1 des Gesetzes vom 18. Juli 2017 (BGBl. I S. 2771) wird -

Gemeinnützige Baugenossenschaft Bergedorf Bille e.G.

erlaubt, an den im beigehefteten Lageplan bezeichneten Stellen des Flurstückes 2109 der Gemarkung Lohbrügge, Dünenweg 74/76

das auf den befestigten Flächen anfallende Niederschlagswasser über eine Rigole zu versickern.

Diese Erlaubnis ist widerruflich und ersetzt nicht Genehmigungsakte, die nach anderen Vorschriften erforderlich sind.

2. Auflagen und Bedingungen:
   2.1. Es darf nur unverschmutztes Niederschlagswasser über die Rigole zur Versickerung gebracht werden.
   2.2. Die Rigole ist gemäß der hydraulischen Berechnung vom 08.10.2018 zu erstellen. Sie muss eine Speicherkapazität von mind. 12,65 m³ aufweisen. Ihre Unterkante darf nicht tiefer als NN 26,7 m liegen.
   2.3. Das auf den Pkw-Stellplätzen und deren Zufahrten anfallende Niederschlagswasser darf nicht direkt in die Rigole eingeleitet werden. Ist eine Versickerung über die belebte Bodenzone (z.B. über angrenzende Grünflächen oder Mulden) nicht möglich, ist das Niederschlagswasser über entsprechend geeignete Reinigungsanlagen vor zu reinigen.
   2.4. Die Rigole ist ständig in einem betriebsfähigen Zustand zu halten. Um ihre Funktionsfähigkeit zu erhalten, ist anfallendes Sediment alle 2 Jahre und nach Bedarf zu entfernen.
   2.5. In mindestens halbjährlichen Zeitabständen sind die der Rigole vorgelagerten Revisionsschächte sowie die vorgeschaltete Reinigungsanlage auf eventuelle Ablagerungen hin zu überprüfen. Ablagerungen wassergefährdender Stoffe (wie z. B.

Internetadresse: www.hamburg.de/bue
Behindertenstellplätze: Zufahrt Neuenfelder Straße 19; Zentrale 428 40-0
S-Bahn 3 bis Wilhelmsburg Buslinie 13 oder 34

Mineralöle, Benzinkohlenwasserstoffe, Teere, schwefelige Chemikalien u. ä. w.), verursachen durch Undichtheiten u. ä., sind unverzüglich der Wasserbehörde anzuzeigen, nach Absprache zu entfernen und erforderlichenfalls zu beseitigen.

2.6. Die Benutzung wassergefährdender Stoffe wie z. B. Lacke, Farben, Lösungsmittel u. ä. auf den an die Versickerungsanlage angeschlossenen Flächen ist untersagt.

2.7. Sollte beim Bau der Versickerungsanlage von der Erlaubnis (Dimensionierung, Anlagentyp, Tiefenlage der Anlagen etc.) abgewichen werden, sind entsprechende Änderungsplanungen mit der Wasserbehörde abzustimmen. Nach Fertigstellung der Versickerungsanlagen ist ein Plan mit der tatsächlichen Abmessungen und der Lage der Versickerungseinrichtungen an die o. g. Anschrift zu senden.

2.8. Beim evtl. Auftreten von Beeinträchtigungen für Nachbargrundstücke behält sich die Wasserbehörde die Anordnung nach weiteren Maßnahmen, z. B. Vergrößerung der Versickerungskapazität, ausdrücklich vor.

3.1. Antrag vom 17.01.2019 (Anlage I.)
3.2. Auszug Liegenschaftskataster M 1 : 1.000 (Anlage I.)
3.3. [illegible] (Anlage I.)
3.4. Erläuterungsbericht (Anlage I.)
3.5. Querschnitt Rigole (Anlage I.)
3.6. Hydraulische Bemessung Rigole (Anlage I.)
3.7. Bewertung nach DWA-M153 (Anlage I.)
3.8. Geotechnischer Bericht und Versickerungsbewertung (Anlage I.)
3.9. Bericht zum Einbau Versickerungsanlage (Anlage I.)

unumerungen wird zu bezahlen!

4. Gebühren:

5. Ihre Rechte:
Gegen diesen Bescheid kann innerhalb eines Monats nach Bekanntgabe Widerspruch bei der im Briefkopf bezeichneten Dienststelle erhoben werden.

- Hella Franz -

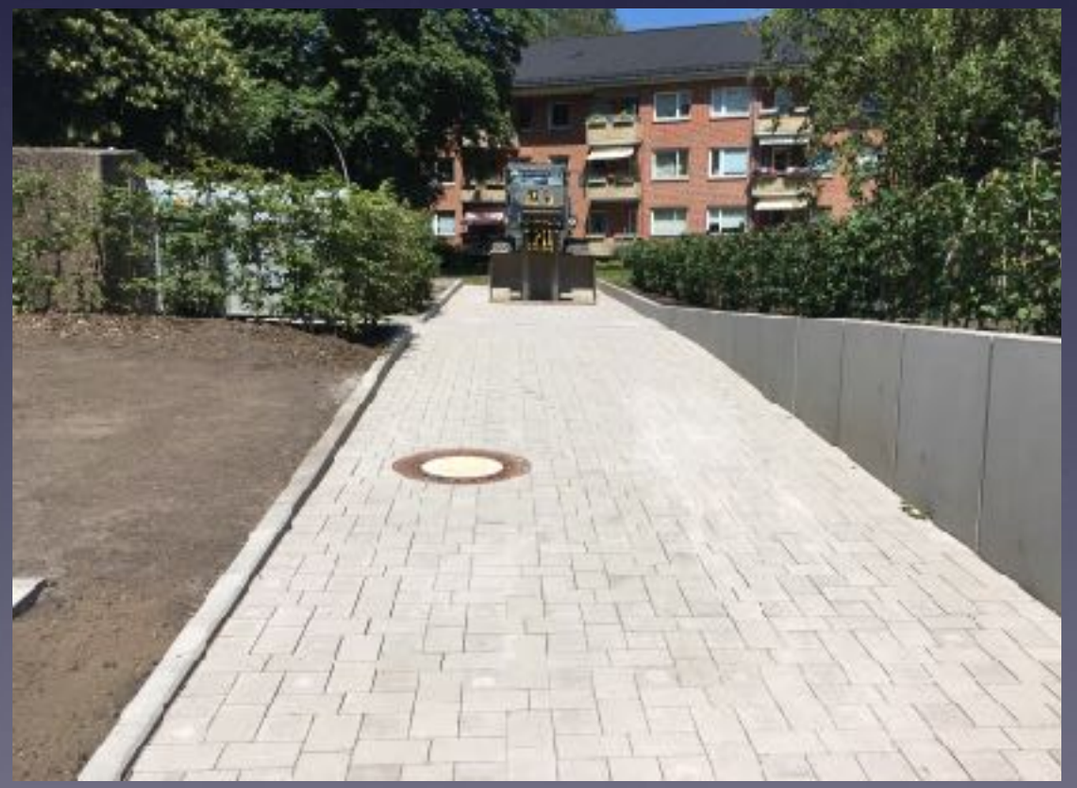

III
74
III
76
Sorbus 'Brouwers'
Crocus tommasinianus 'Rudy Giant'
Linde
Vorgarten-beet
Eibe
Mietergärten
Poller-leuchte
Quadroton 60x40x8cm
Natura 21x14x8cm
Chinodoxa luciliae
Prunus 'Accolade'
Rasen
Mast-leuchte
Waben-pflaster
Hainbuchenhecke
Müllplatz
Natura 21x14x10cm
Hainbuchen-hecke
Mietergärten
Rasen
Mietergärten
Eibe
Malus 'Evereste'
Rosa spinosissima
CC-Grenze
Narcissus triandrus 'Petrel' in Tuffs
Quadratpflaster anthrazit, 20x20x8cm
Feuerwehrzufahrt
Trockenrasen
Narcissus triandrus 'Petrel' in Tuffs
Maschen-drahtzaun
CC-Grenze
Hasel
Cornus 'Midwinter Fire'
Bergedorf Bille
Gemeinnützige Baugenossenschaft eG
Dünenweg 74 / 76
Revisionsplan
Planstand: 17.12.2019
Bearbeitung: St / Sch
M 1:100
SPALINK-SIEVERS Landschaftsarchitekten
Alte Herrenhäuser Str. 28
30419 Hannover
Tel. 0511 979 259 - 0
www.spalink-sievers.de

Projekt Dünenweg 74/76
Beseitigung der Schäden nach Starkregenereignis 2018

- Bauzeit: Februar - Juni 2019, Pflanzung Nov. 2019

- Baukosten brutto/brutto: 395.000 €

- Grundstücksfläche ohne Gebäude: 1.200qm

- Netto Baukosten € 155,50/qm

Projekt Ladenbeker Furtweg 6/8 und Dünenweg 21 - 25

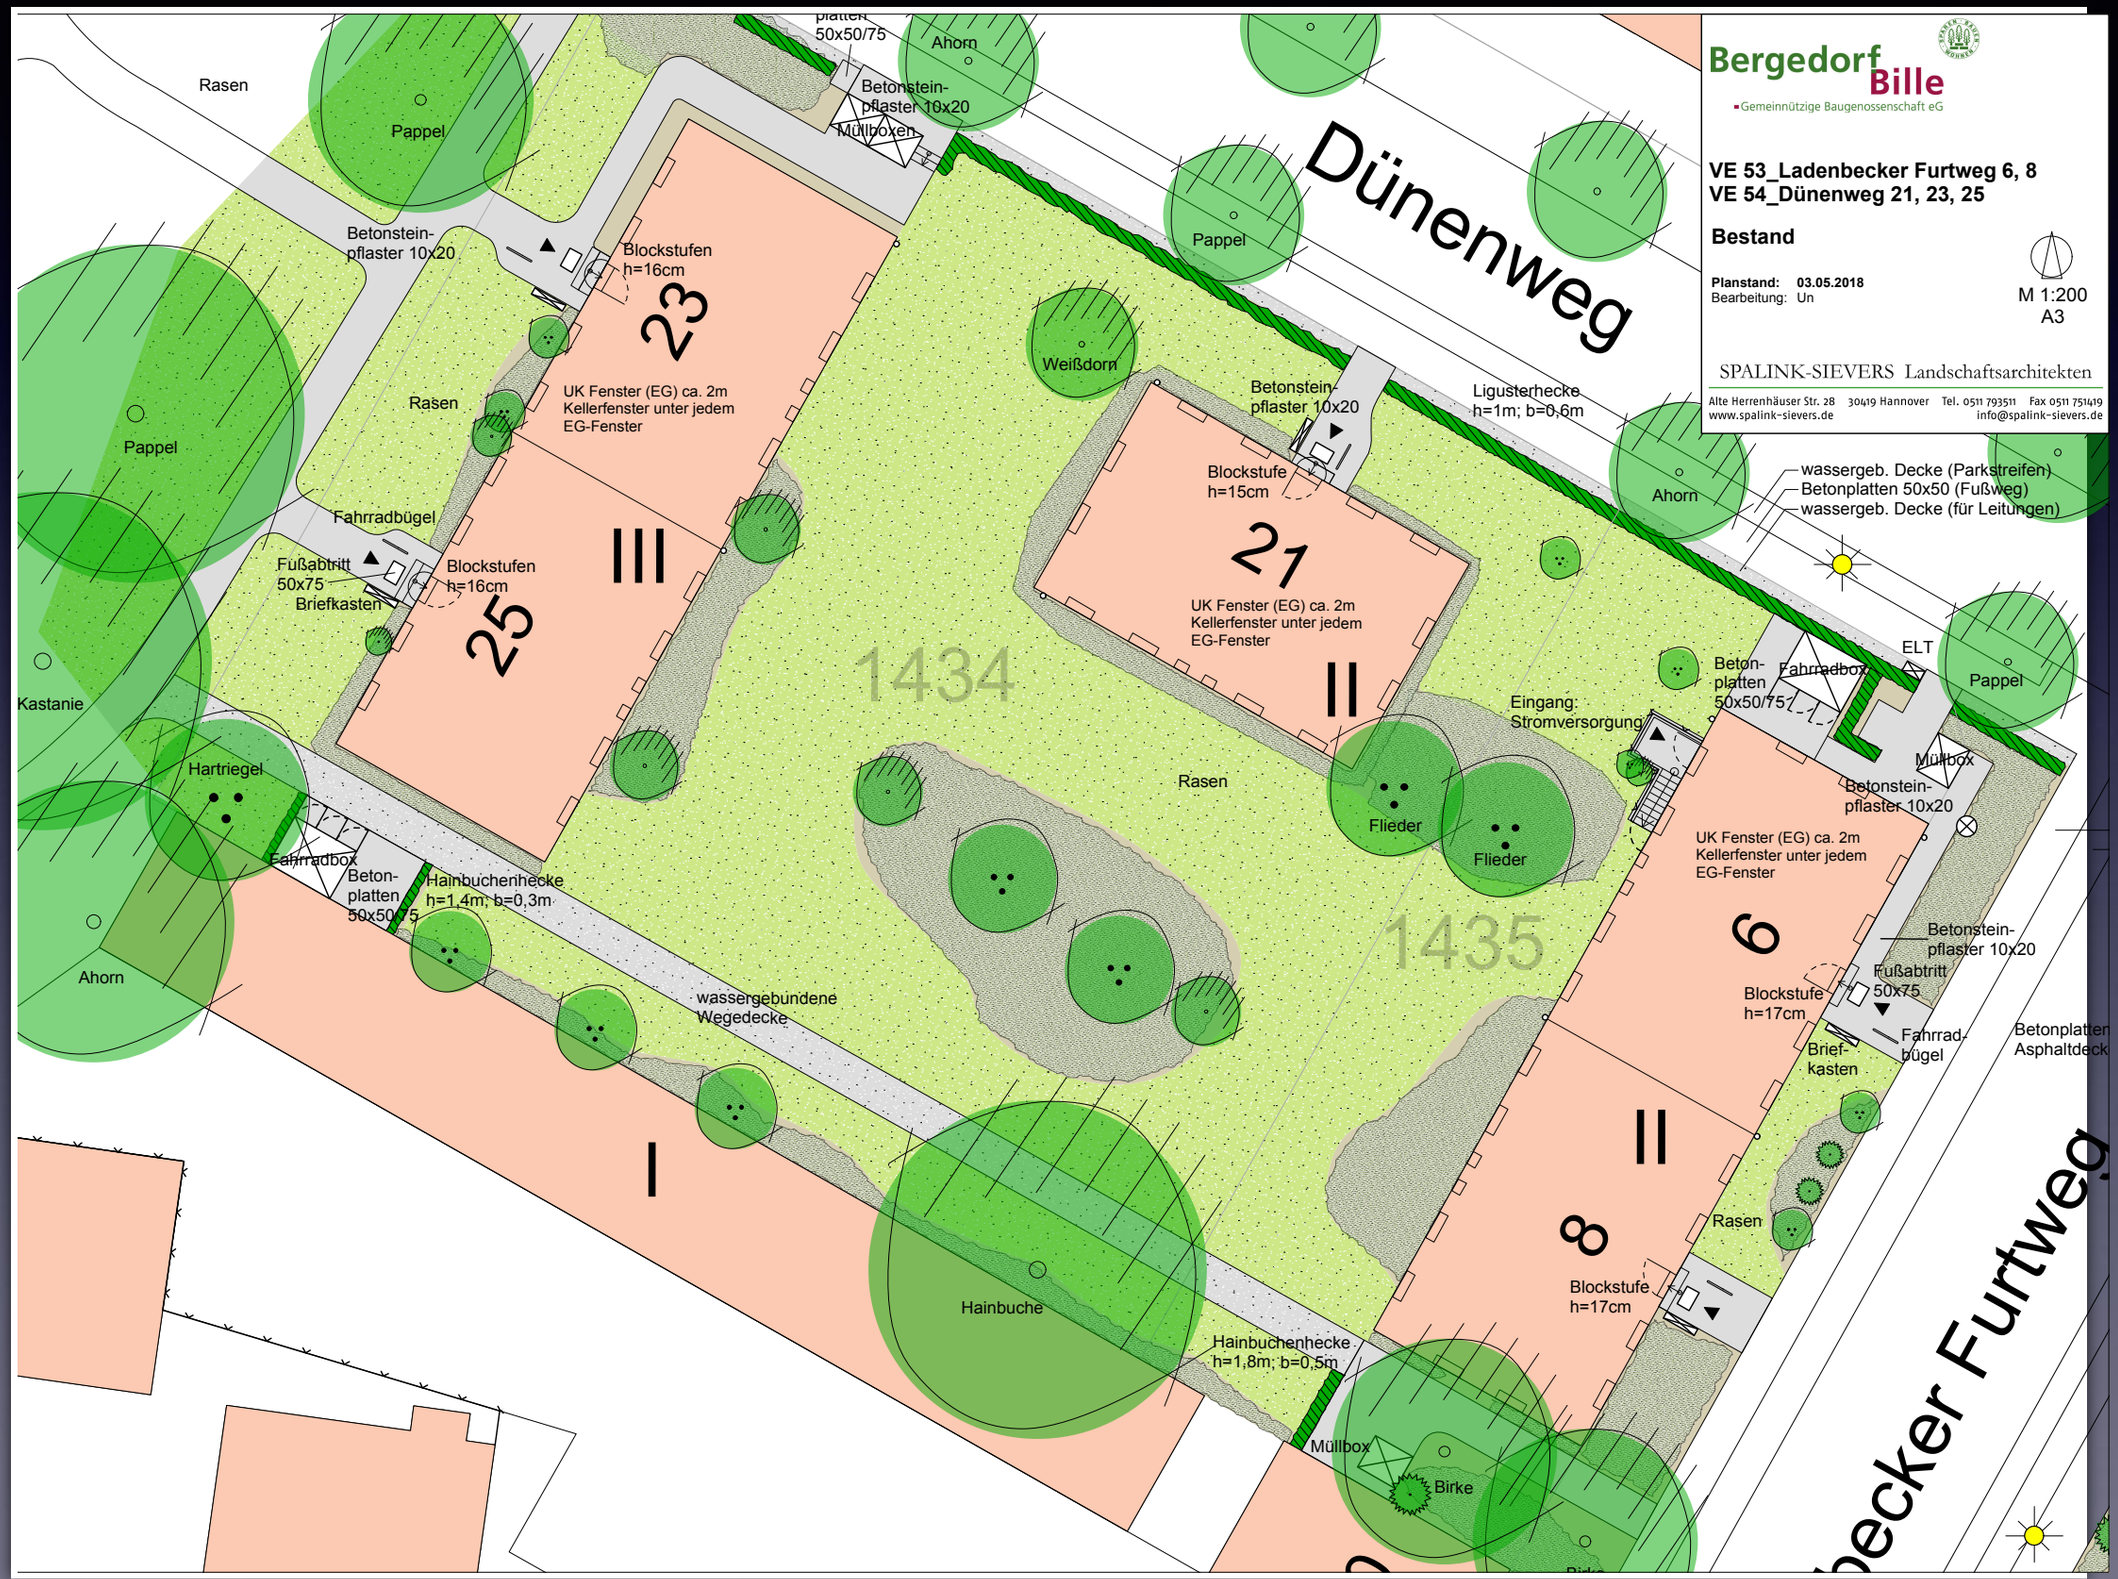

Zustand der Gebäude und der Außenanlagen vor der Sanierung der Fassaden

Dünenweg

23
II

21
II

6
II

25
II

8
II

Ladenbeker Furtweg

Neugestaltung der Aussenanlagen Ladenbeker Furtweg 6/8 und Dünenweg 21 - 25 nach der Sanierung der Gebäude

- Bauzeit September 2020 bis Februar 2021

- Baukosten brutto/brutto 163.000 €, davon 25.500 € für die Regenwasserversickerung (Füllkörperrigolen, Mulden, Rinnen,Leitungsarbeiten, etc)

- Grundstücksfläche ohne Gebäude 1.670 qm

- Baukosten netto € 73,50/qm

Geplante Quartiersentwicklung Dünenweg

Bergedorf Bille
Gemeinnützige Baugenossenschaft eG

Quartiersentwicklung Dünenweg

Freianlagen - KONZEPT

Planstand: 28.03.2023
Bearbeitung: St

o.M.
DIN A3

SPALINK-SIEVERS LandschaftsArchitekten PartG
Alte Herrenhäuser Str. 28
30419 Hannover
Tel. 0511 979 259 – 0
www.spalink-sievers.de

Geplante Quartiersentwicklung Dünenweg

- Energetische Sanierung der Gebäude und der Wärmeversorgung, Schließung der Kellerabgänge, Bau von Fahrradhäuschen
- Höhengerechte Erschließung der Hauseingänge und Erneuerung/Ergänzung des Wegenetzes
- Anlage von Mietergärten zur barrierearmen Erschließung der EG-Wohnungen auf der Rückseite
- Anlage von kindgerechten Spielplätzen
- Schaffung von Gemeinschaftsflächen(Bänke, Hochbeete)
- Erneuerung der Müllplätze, wo möglich als Unterfluranlagen
- Anlage von Blühflächen und klimaverträglichen Neupflanzungen
- Anlage von Versickerungsmulden in Kombination mit Füllkörperrigolen zur Sammlung des Oberflächen- und Dachwassers zur Entlastung der öffentlichen Siele

Beispiele für Fahrradhäuschen und Terrassengärten

Vielen Dank für Ihre Aufmerksamkeit

www.spalink-sievers.de